
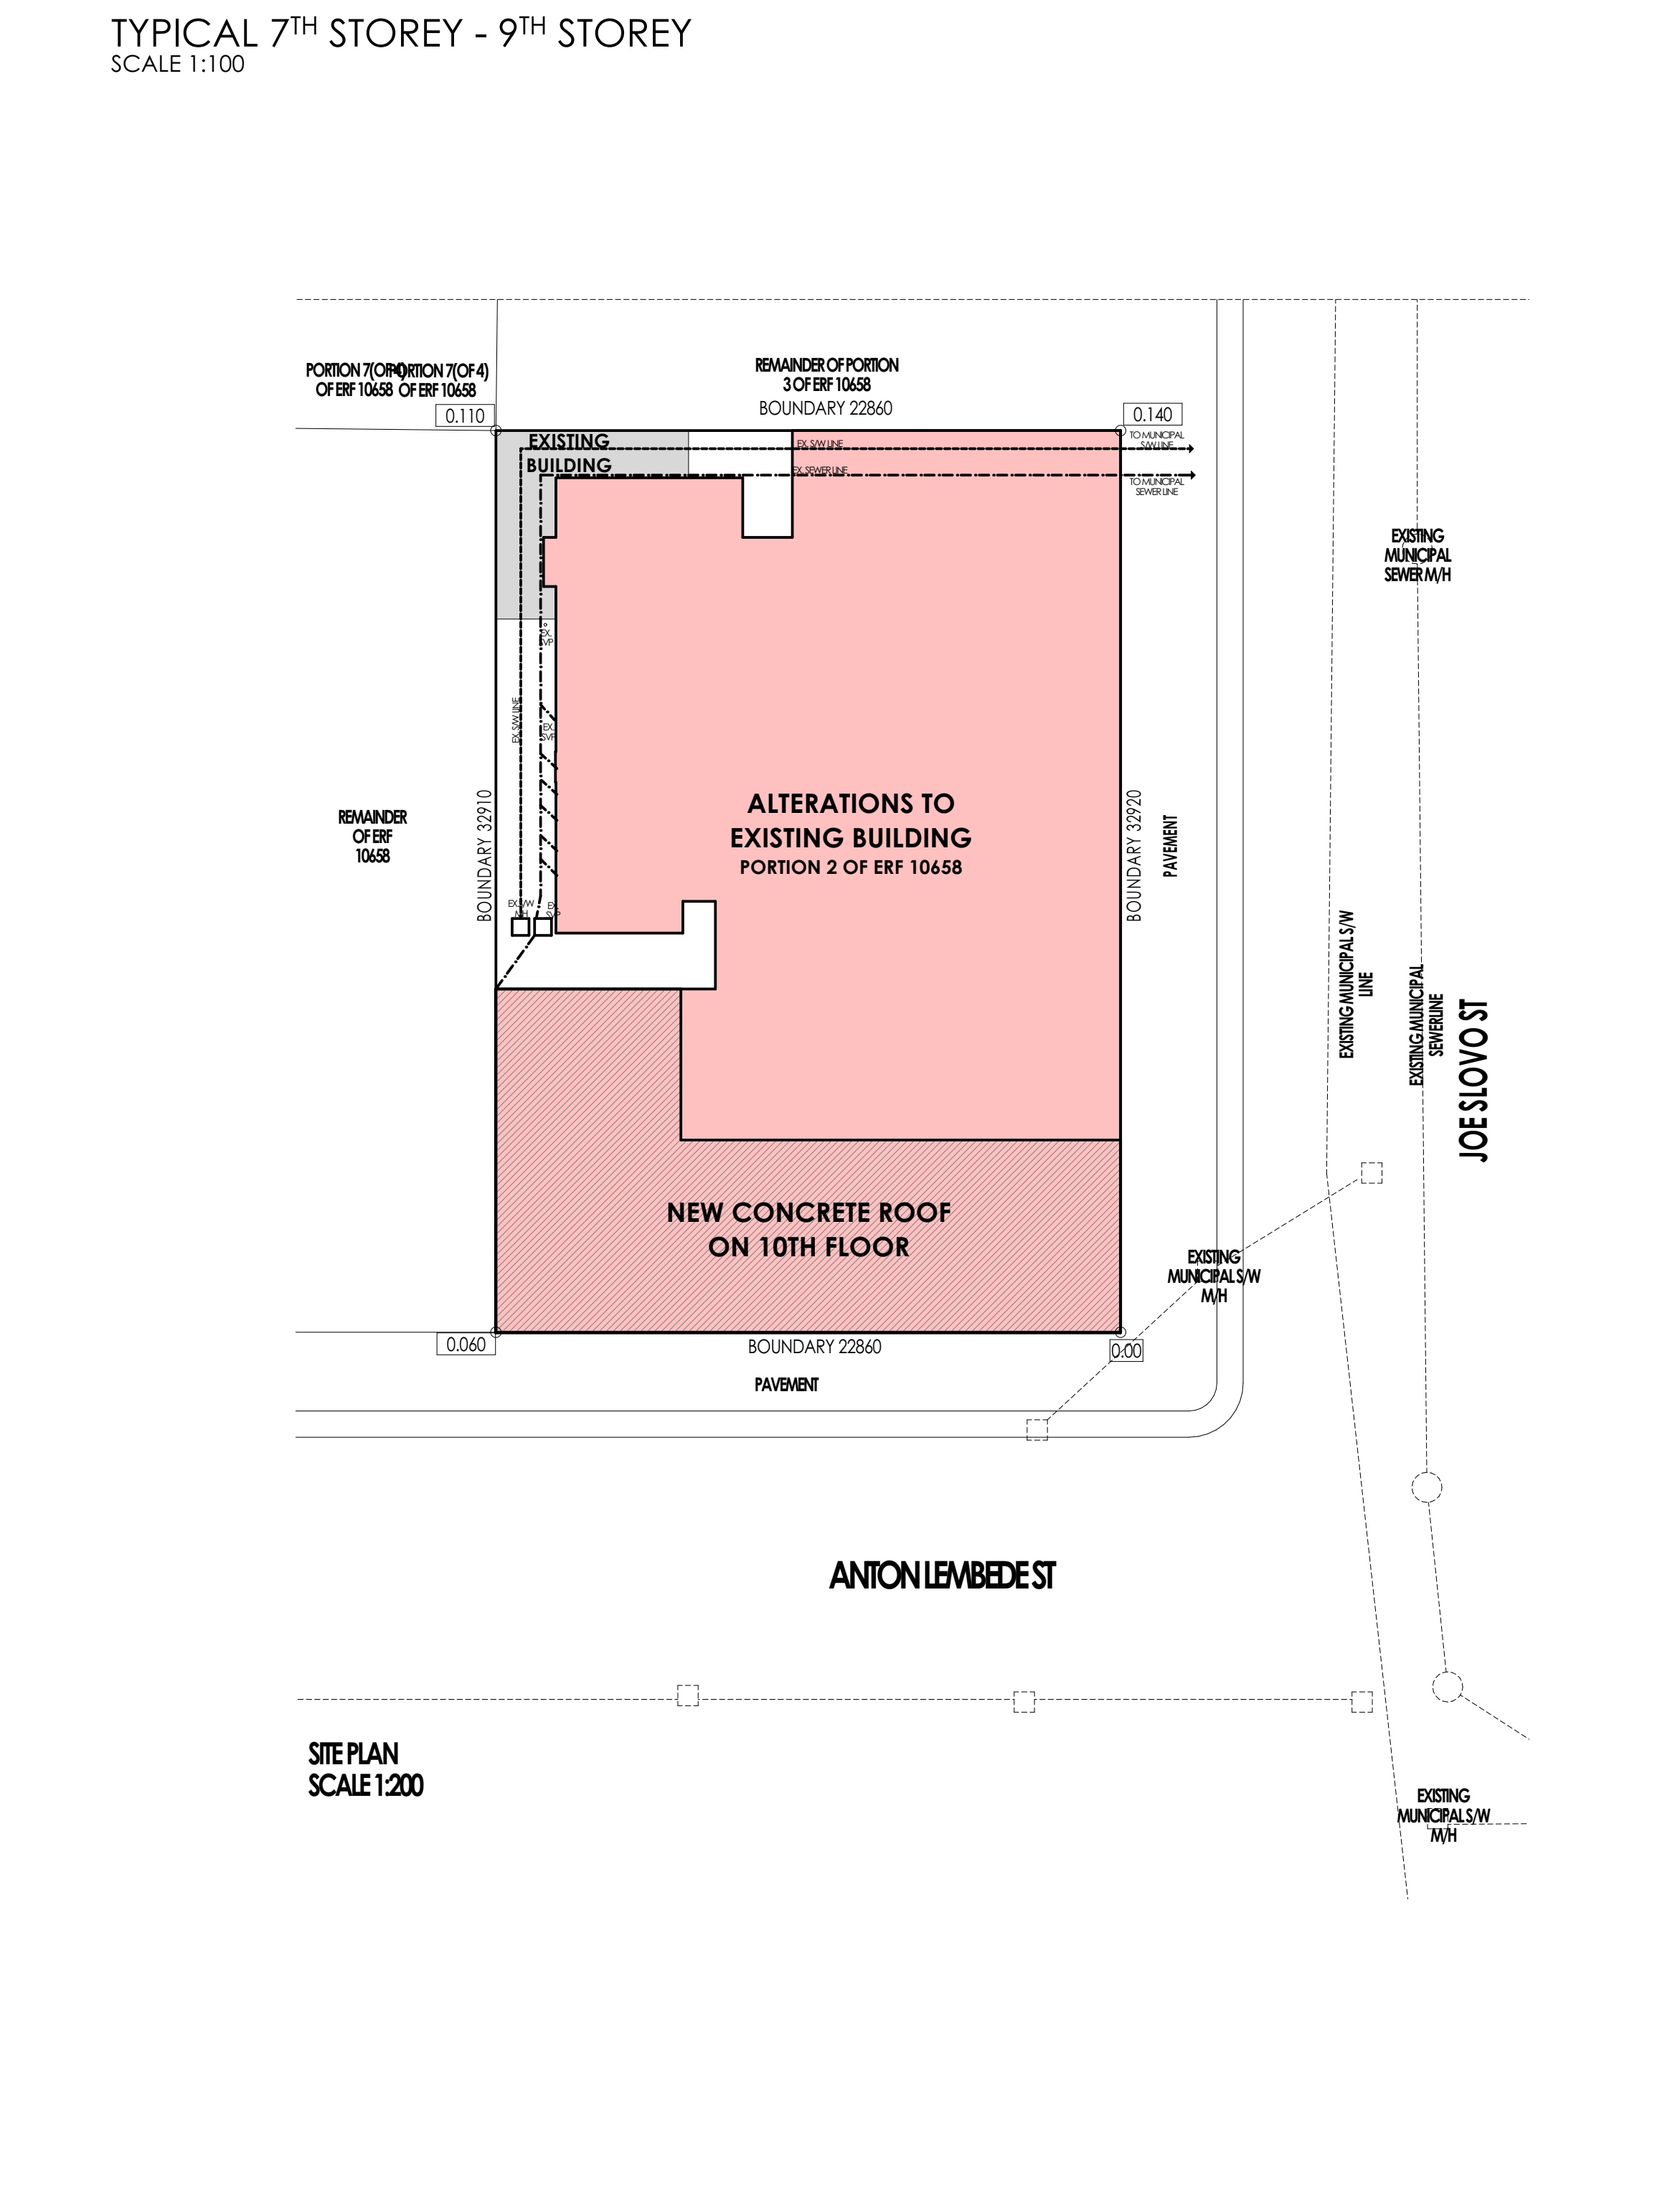


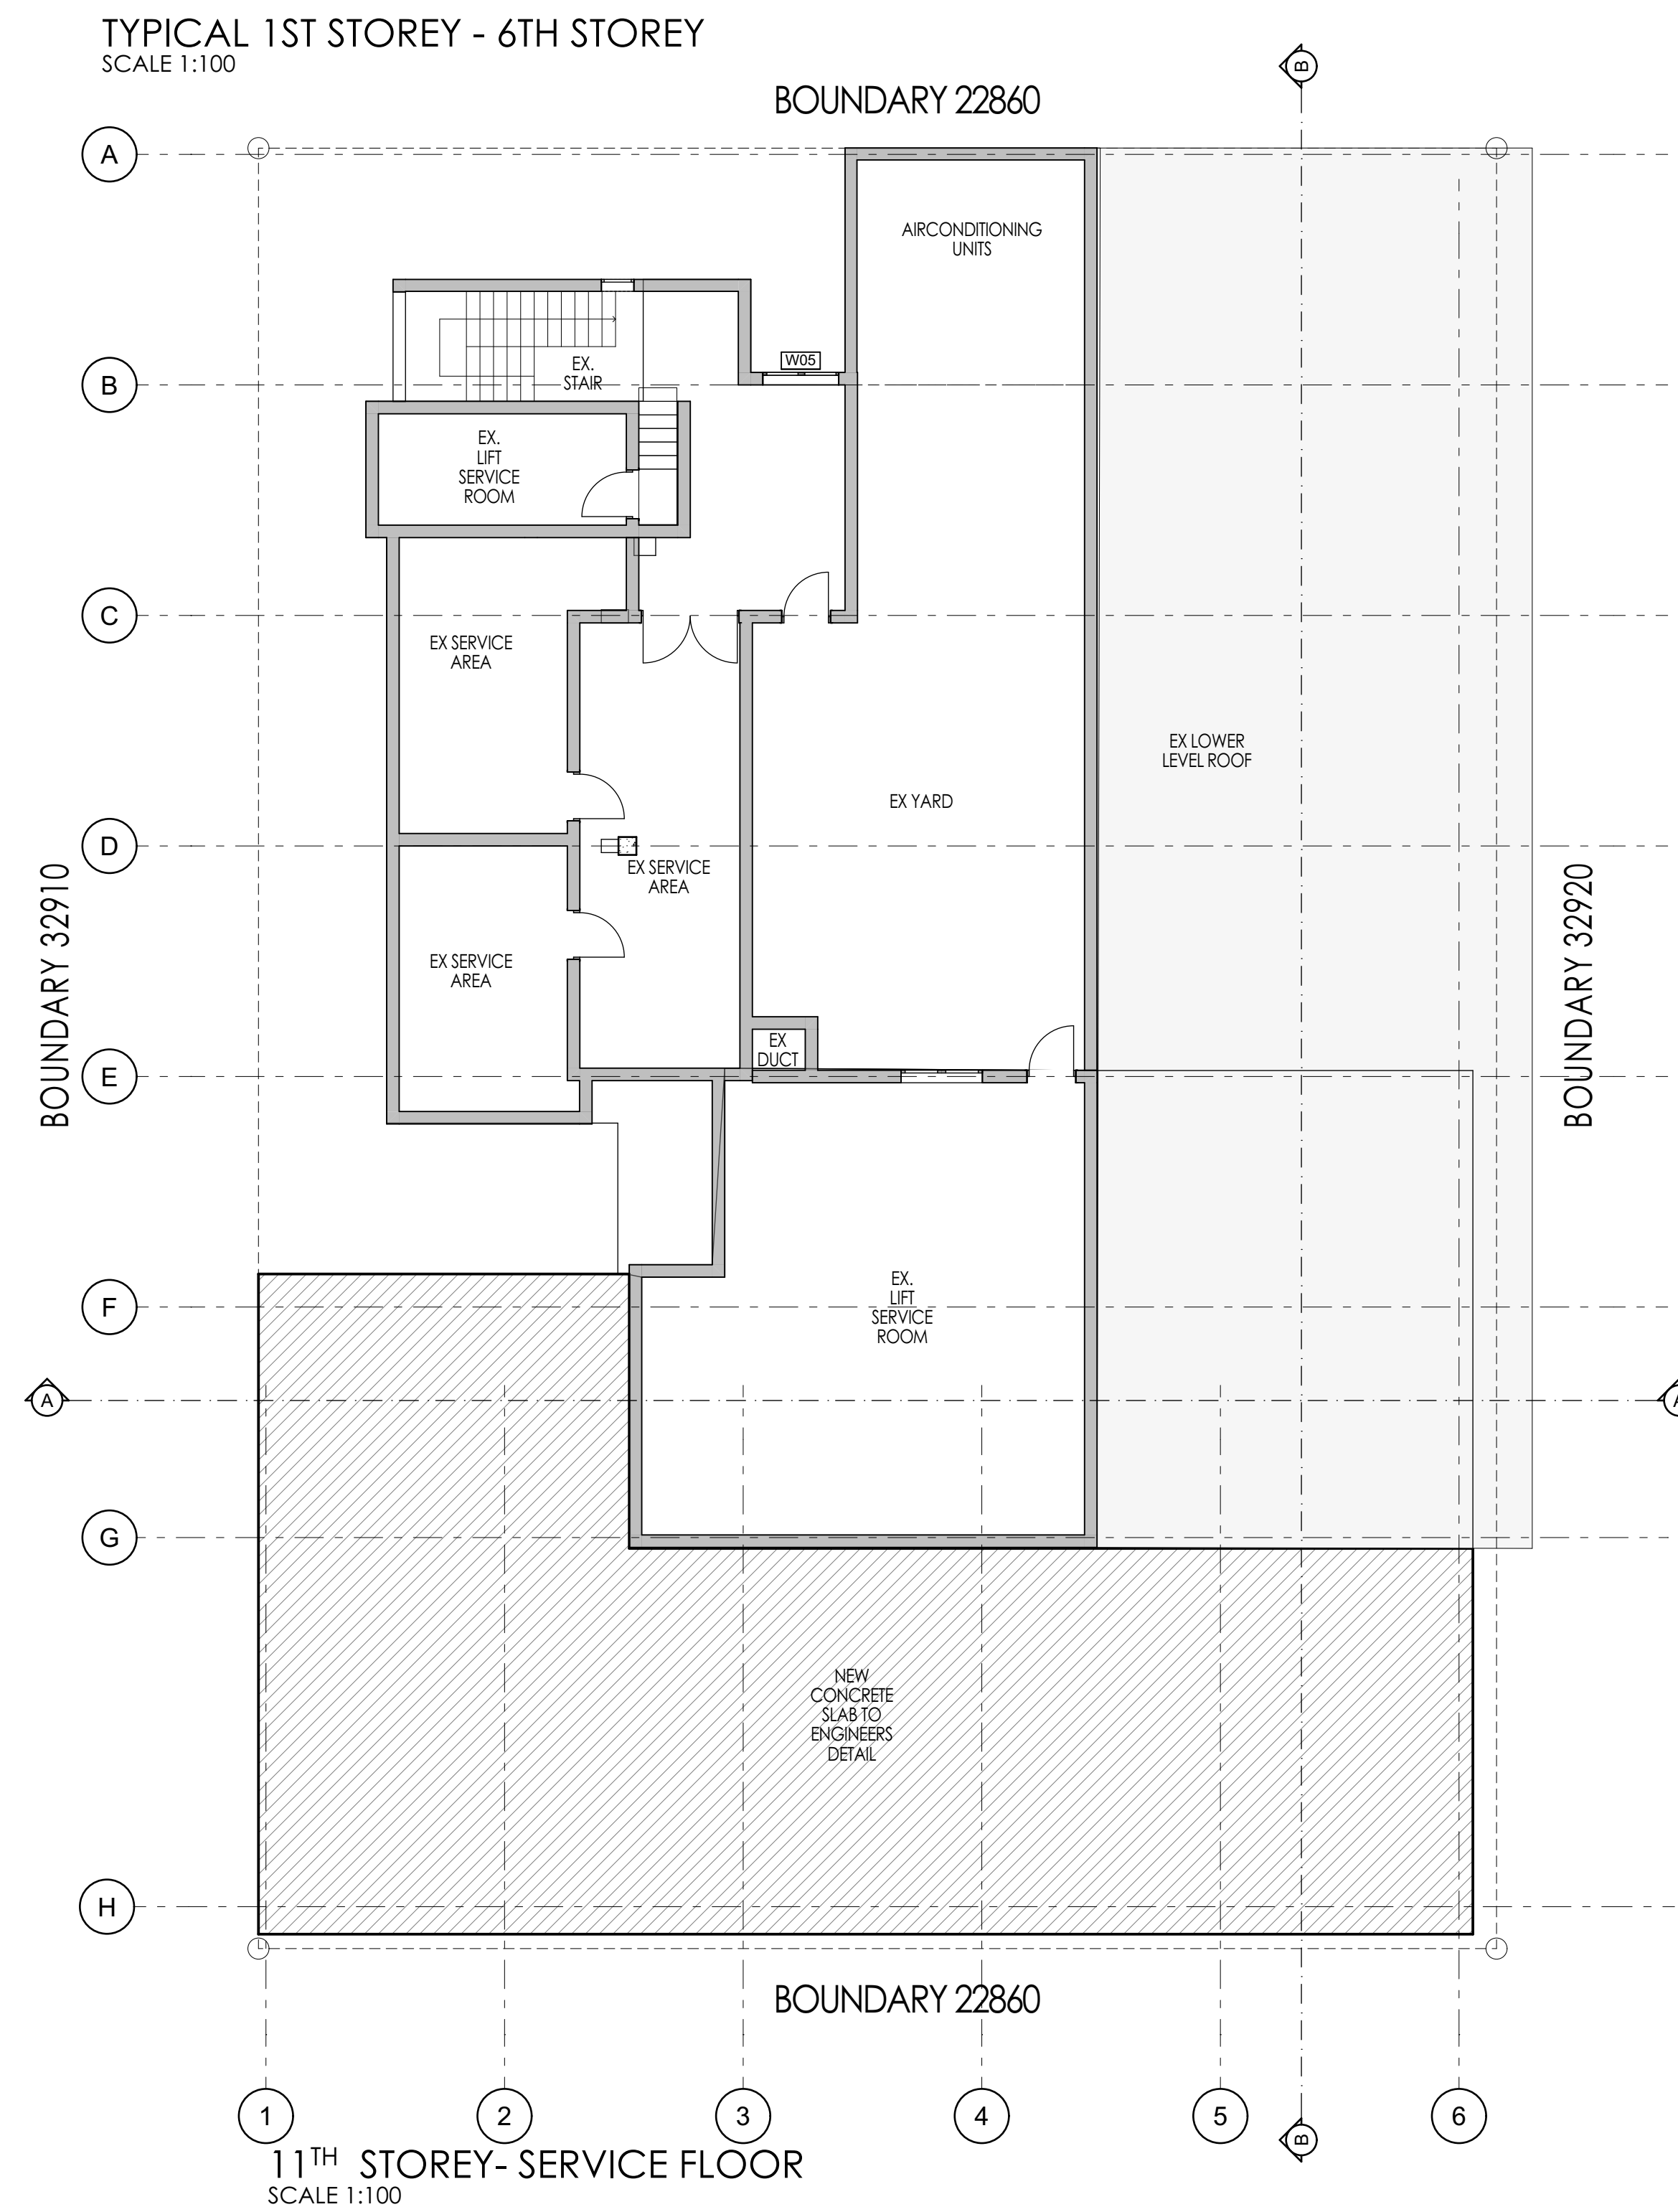

- ## WINDOW & GLAZING
1. Window frames to be bronze powder coated and finish over with bronze powder paint.
 2. All windows and manufacturing to be comply with SAGGA / AAMA/ASA requirements / regulations.
 3. All windows to have tape protection
 4. All glazing to be in accordance with NBR 0400.
 5. Glazing to bathrooms and WC's to be in opaque glass.
- ## SITING AND EXCAVATION
1. All boundary bescoments to be flagged by a registered land surveyor. Contractor to obtain a certificate stating that work has been completed and set out prior to commencement of excavations.
 2. The contractor is to check all dimensions and levels before commencing work, and to report any discrepancies to the Architect.
 3. Contractor is to confirm and ensure the correctness of finished floor and external levels physically on site with Local Authority inspector before commencement of construction
 4. If the site is found to contain clay, shale groundwater or any suspect soil conditions, the foundations are to be to professional engineer's specification and supervision, and will supersede the specifications stated on this plan.
- ## LOCAL AUTHORITY
1. The owner is responsible for all Local Authority notices and fees.
 2. The owner is required to obtain all necessary consents to services
 3. Where necessary and feasible, all building regulations require more stringent specifications than what is shown herein, they are to be followed with prior consultation to the owner.
 4. The contractor is to inspect the official approved copies of the drawing to ensure that all amendments have been taken into account.
 5. All SANS 10400 specifications and SABS standards to be applied, and to use minimum standard and recommended construction principles.
 6. All areas above and below stairs are approximate and must be verified.

SCHEDULE OF AREAS	
ZONING: BUSINESS GENERAL, CENTRAL AREA	
OCCUPANCY: BOARDING HOUSE	
AREA OF SITE	753 m ²
PERMITTED COVERAGE	N/A
PERMITTED F.A.R. (8.0)	6024 m ²
EXISTING F.A.R. (-)	- m ²
PROPOSED F.A.R. (-)	- m ²
TOTAL F.A.R. (-)	- m ²
EXISTING COVERAGE 0.0%	- m ²
PROPOSED COVERAGE 0.0%	- m ²
TOTAL COVERAGE 0.0%	- m ²
COVERAGE IN HAND	- m ²
F.A.R. IN HAND	- m ²
NEW BUILDING AREA (fee calculation)	- m ²

FOR INFORMATION ONLY

ARCHITECT IS TO BE NOTIFIED PRIOR TO COMMENCEMENT OF ANY BUILDING WORKS ON SITE.

CAPACITY CLASSIFICATION:
LABEL

OWNER:

ARCHITECT: Laia Tickley **SACAP REG NO:** 21560

PROJECT
STUDENT ACCOMMODATION ON POR 2 OF ERF10658
DURBAN AT 353 ANTON LEMBEDE STREET DURBAN OF
EAFLEY

TITLE
FLOOR PLANS

JOB NO.	DATE	DRAWN
LTK_2017	2022/08/12	ST / LT

DRAWING NO.	REVISION NO.	SCALE
LA-100		1:100, 1:200

consultant (architectural)




LTK
LAWSON TUCKER
ARCHITECTS

072 808 5059

 laia@ltharchitects.co.za

 ltharchitects.co.za

 4 Ribbon Place
Morningside
Durban
4000

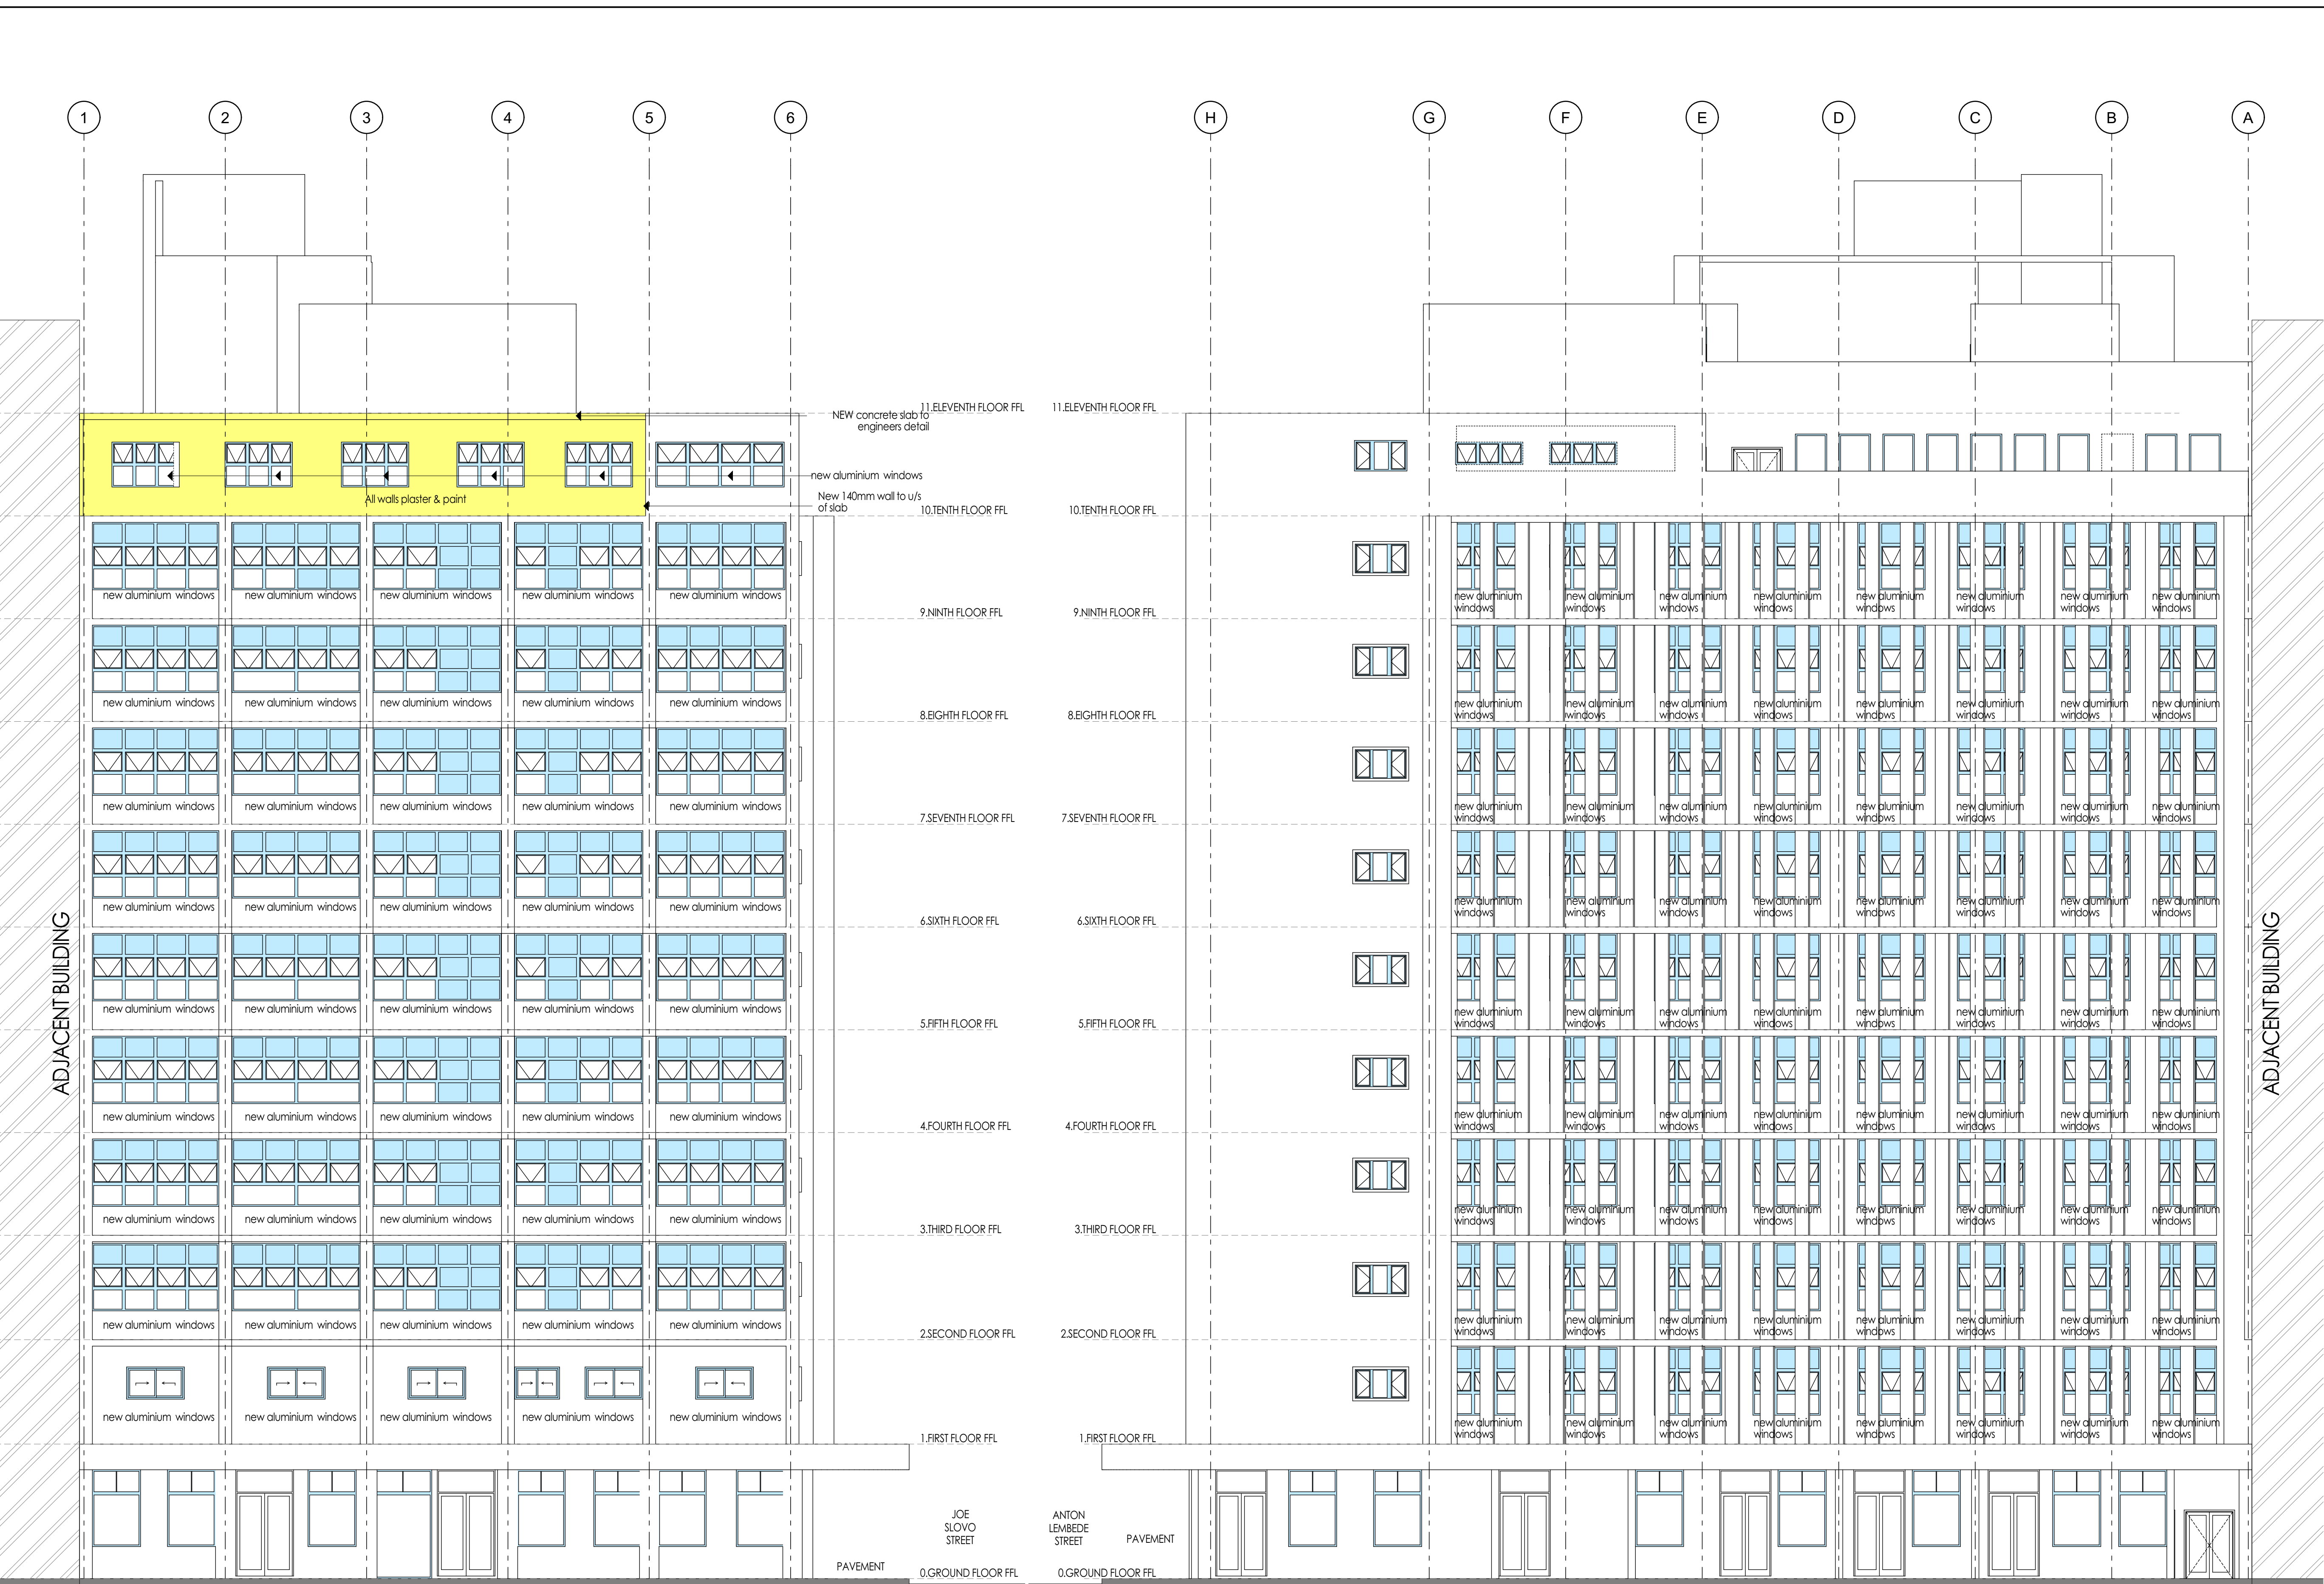

NORTH ELEVATION
SCALE 1:100

WEST ELEVATION
SCALE 1:100

FOR INFORMATION ONLY

ARCHITECT IS TO BE NOTIFIED PRIOR TO
COMENCEMENT OF ANY BUILDING WORKS ON SITE.

OCCUPANCY CLASSIFICATION:
BOARDING HOUSE

OWNER:

ARCHITECT: Laila Tickley **SACAP REG NO:** 21560

THE SOUTH AFRICAN COUNCIL FOR THE ARCHITECTURAL PROFESSION

PROJECT
STUDENT ACCOMODATION ON POR 2 OF ERF10658
DURBAN AT 353 ANTON LEMBEDE STREET DURBAN OF
E ALLY

TITLE
COUNCIL SUBMISSION

JOB NO.
LTK 207_353

DATE
2026/08/12

DRAWN
ST /LT

DRAWING NO.
LA-101

REVISION NO.

SCALE
1:100

consultant (architectural)

LTK


ltkarchitects

072 808 5909


laila@ltkarchitects.co.za

ltkarchitects.co.za

4 Albion Place
Morningside
Durban
4000

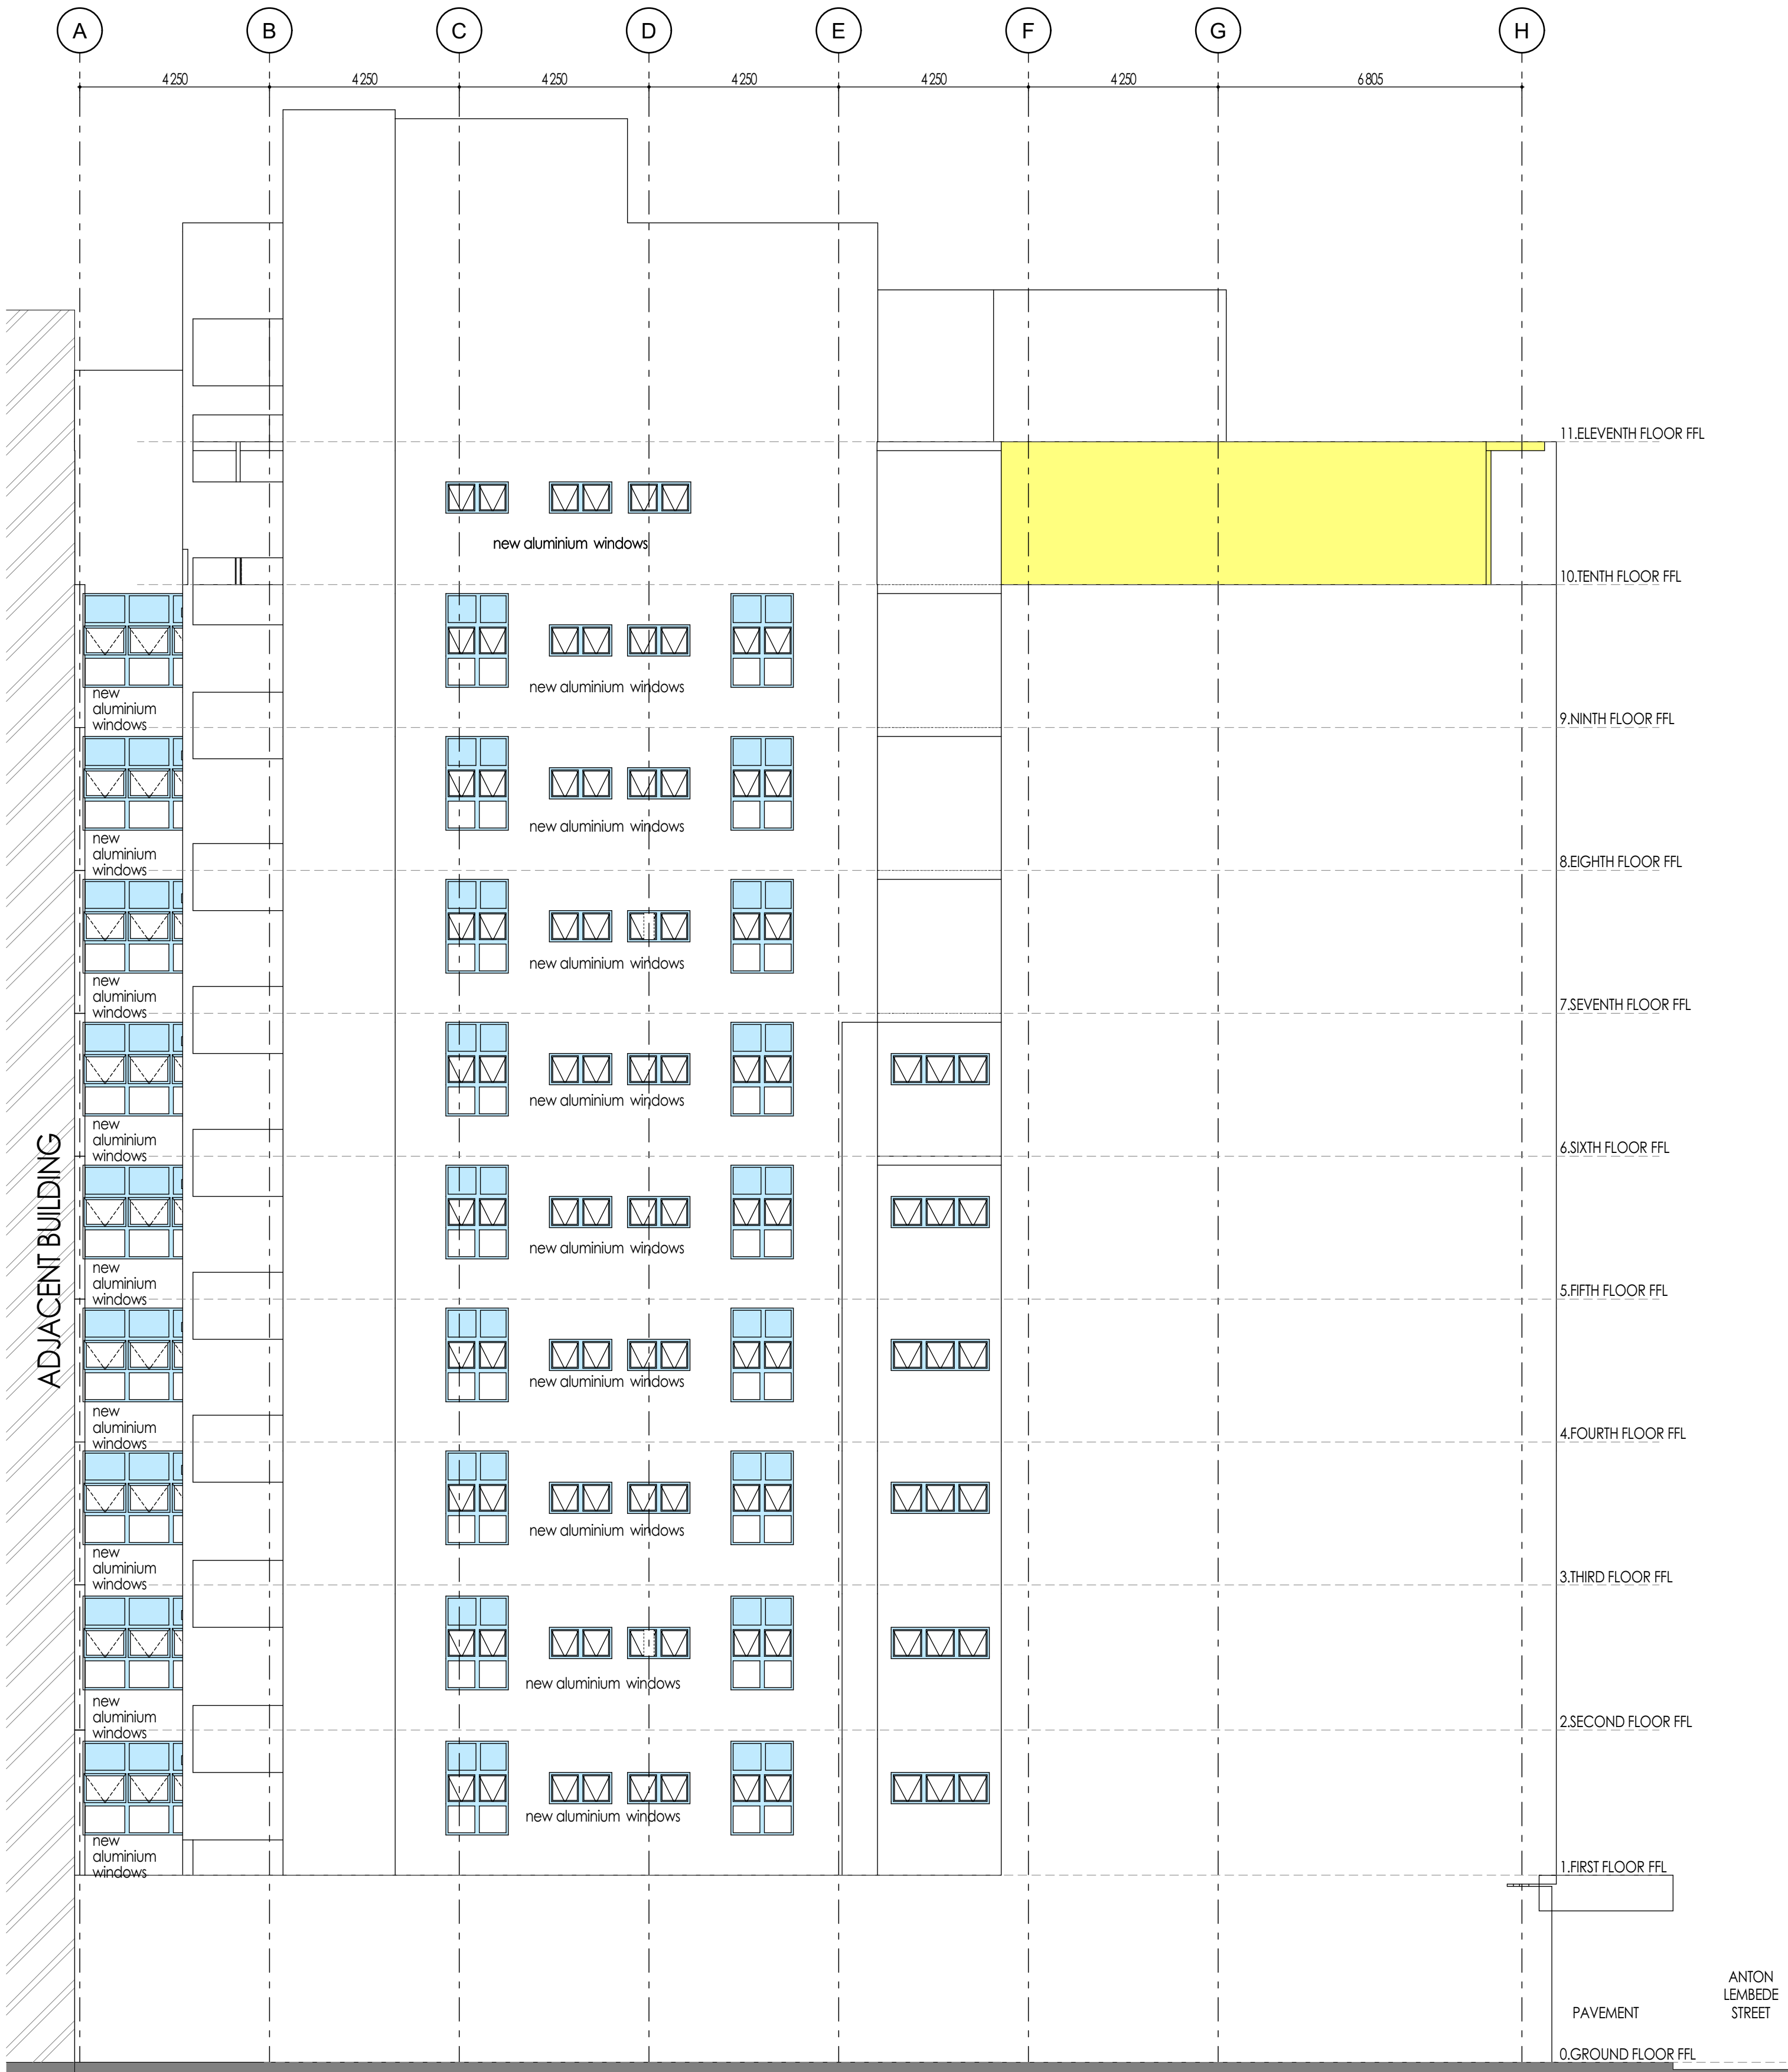

EAST ELEVATION
SCALE 1:100

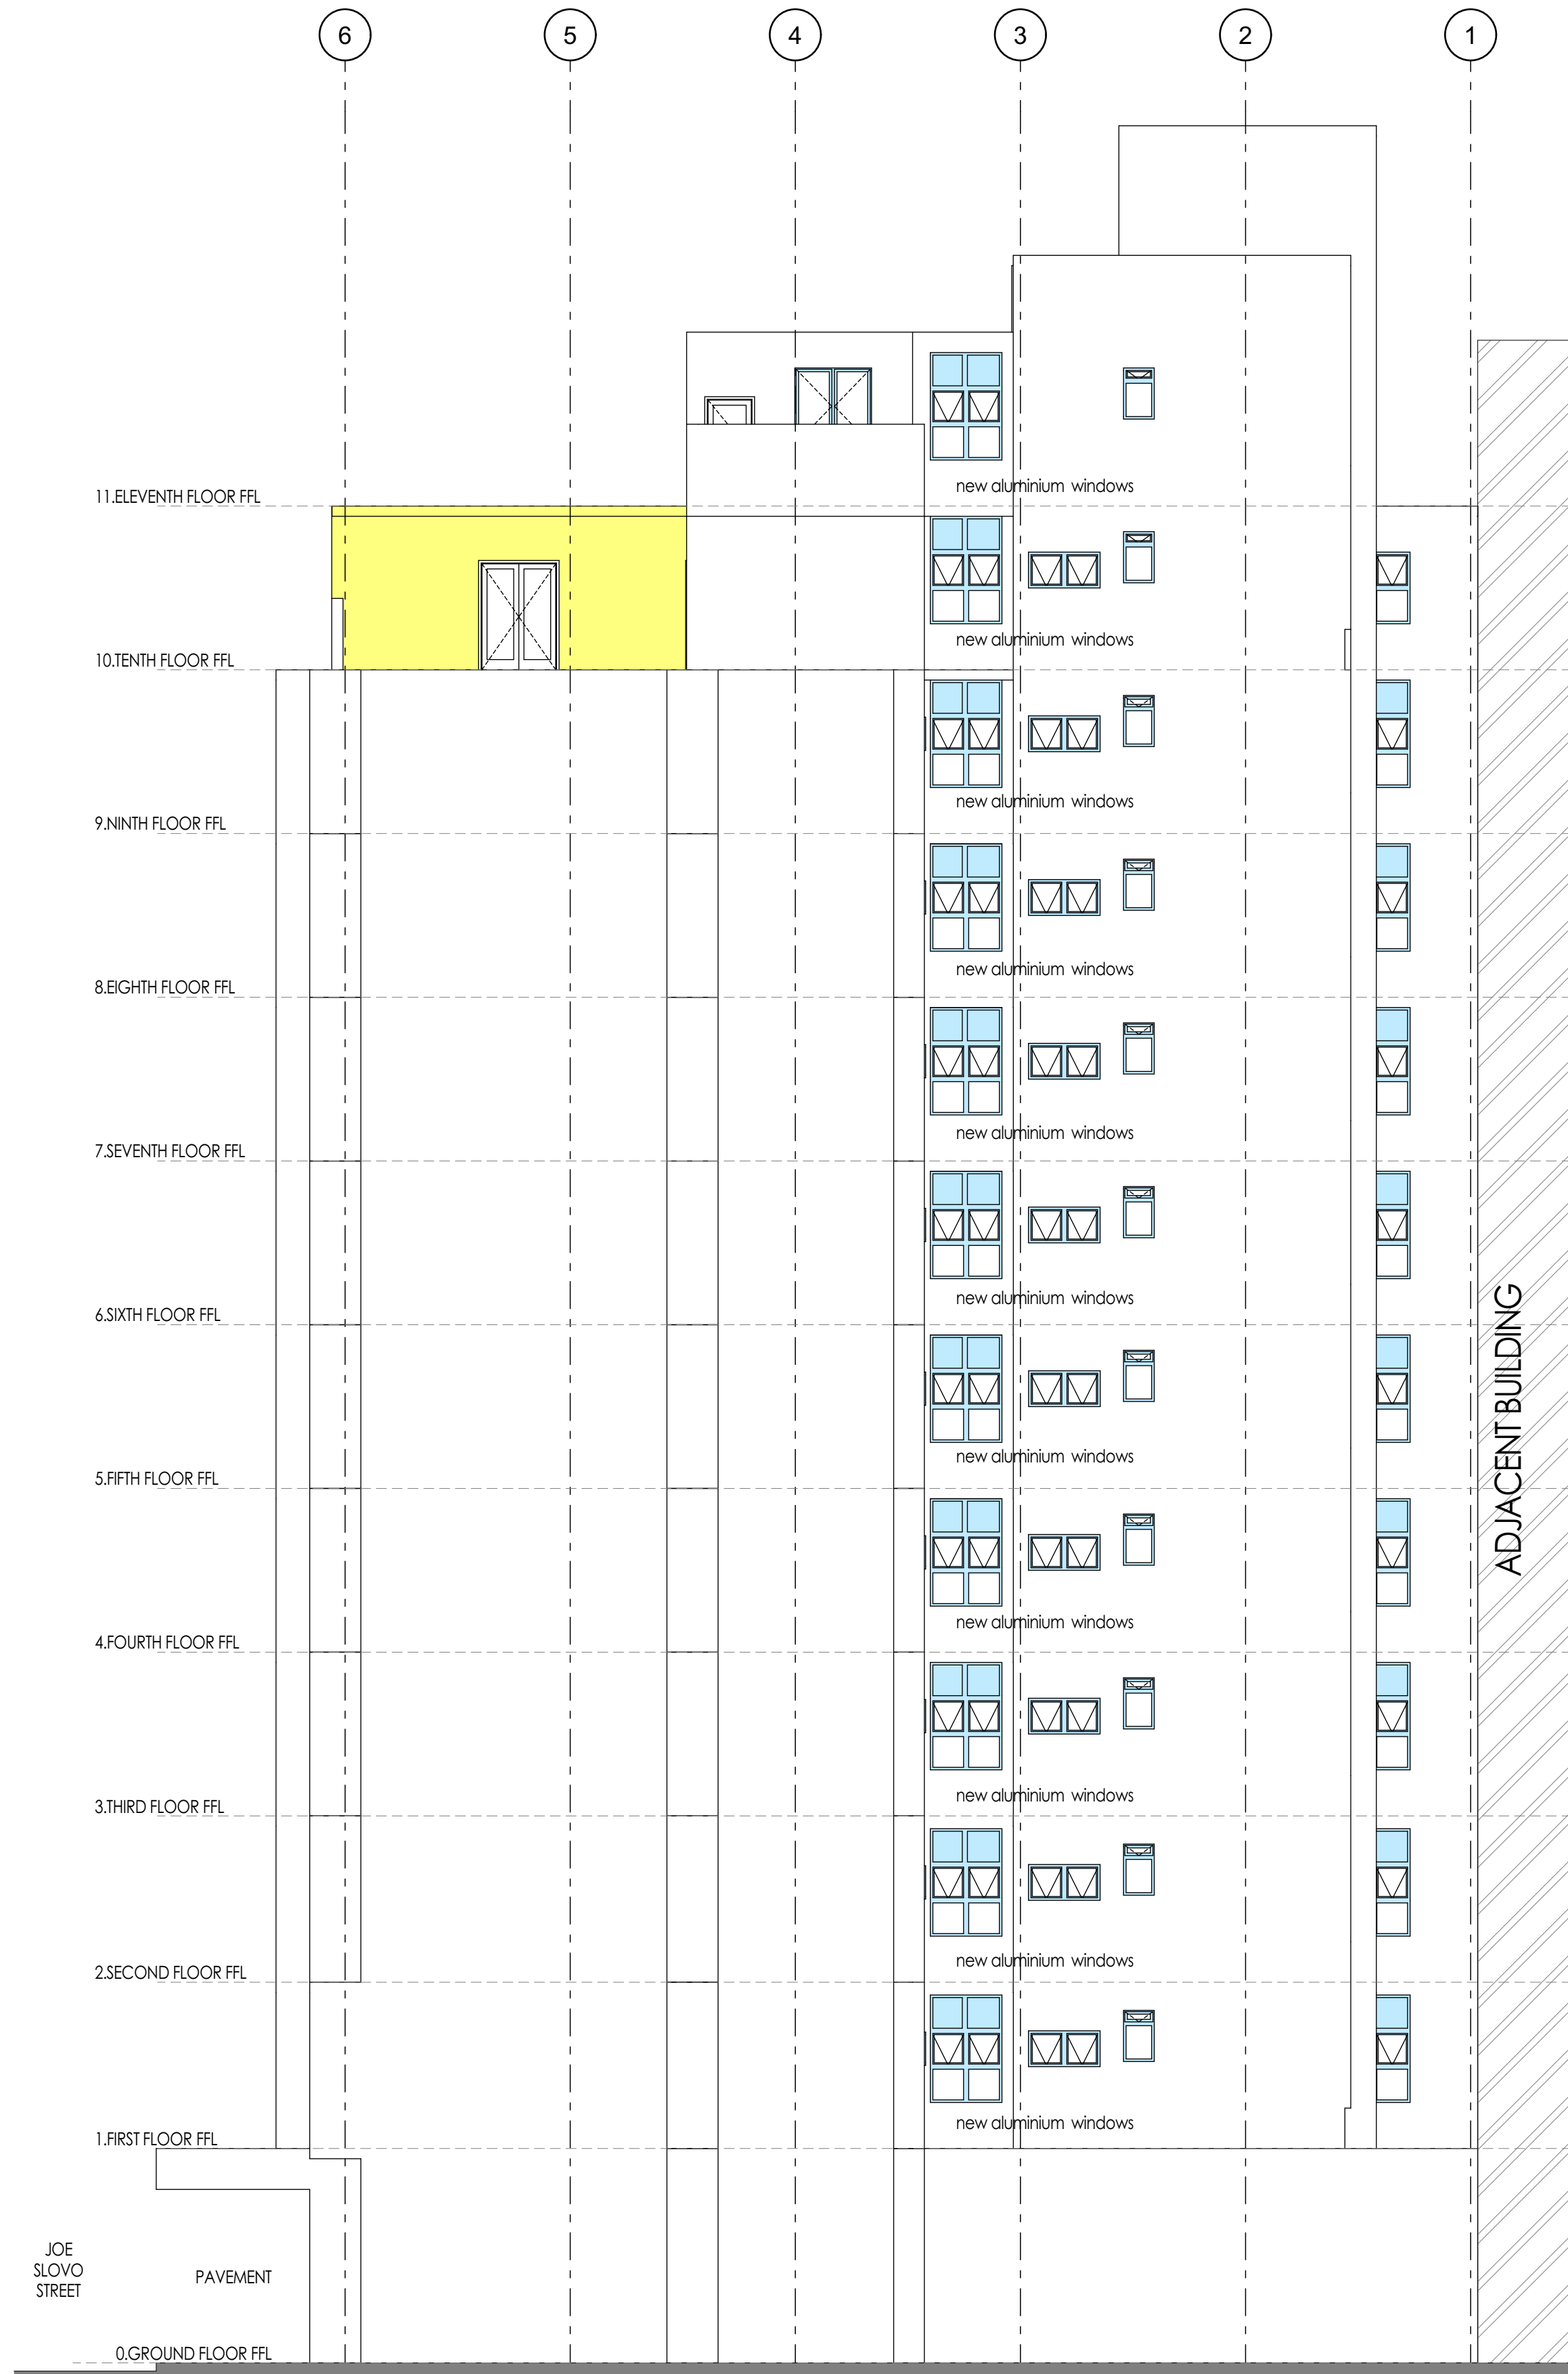

SOUTH ELEVATION
SCALE 1:100

FOR INFORMATION ONLY

ARCHITECT IS TO BE NOTIFIED PRIOR TO
COMENCEMENT OF ANY BUILDING WORKS ON SITE.

OCCUPANCY CLASSIFICATION:
BOARDING HOUSE

OWNER:

ARCHITECT: Laila Tickley **SACAP REG NO:** 21560

THE SOUTH AFRICAN COUNCIL FOR THE ARCHITECTURAL PROFESSION

PROJECT
STUDENT ACCOMODATION ON POR 2 OF ERF10658
DURBAN AT 353 ANTON LEMBEDE STREET DURBAN OF
E ALLY

TITLE
COUNCIL SUBMISSION

JOB NO. LTK 207_353	DATE 2026/08/12	DRAWN ST /LT
DRAWING NO. LA-102	REVISION NO.	SCALE 1:100

consultant (architectural)

LTK
LTK ARCHITECTS

072 808 5909
laila@ltkarchitects.co.za
ltkarchitects.co.za
4 Albion Place
Morningside
Durban
4000



SECTION A-A
SCALE 1:100



SECTION B-B
SCALE 1:100

WINDOW SCHEDULE	
ELEVATION	      
WINDOW NO.	W01
SIZE (W x H)	1800 x 1000
FRAME	MB-Aluminum, New
GLAZING	Single-Glass
WINDOW NO.	W02
SIZE (W x H)	3940 x 2100
FRAME	MB-Aluminum, New
GLAZING	Double-Glass
WINDOW NO.	W03
SIZE (W x H)	4900 x 2100
FRAME	MB-Aluminum, New
GLAZING	Double-Glass
WINDOW NO.	W04
SIZE (W x H)	4900 x 2100
FRAME	MB-Aluminum, New
GLAZING	Double-Glass
WINDOW NO.	W05
SIZE (W x H)	1400 x 700
FRAME	MB-Aluminum, New
GLAZING	Double-Glass
WINDOW NO.	W06
SIZE (W x H)	1800 x 1000
FRAME	MB-Aluminum, New
GLAZING	Double-Glass